



ABDELRHMAN MOHSEN

BIM ARCHITECT & COORDINATOR

architect.abdelrhmanmohsen@gmail.com

[linkedin.com/in/abdelrhman-mohsen-bimarchitect](https://www.linkedin.com/in/abdelrhman-mohsen-bimarchitect)

PORTFOLIO

2026

BIM WORK

Floor Plans · 3D · Exploded · Sections · Details · BOQ · Families · Navisworks · Clash · CDE

EXTERIOR DESIGN

Contemporary · Classical · Compounds · Master Plans

INTERIOR DESIGN

Luxury Residential · Hospitality · Contemporary

EGYPT EG

UAE AE

SAUDI SA

QATAR

Professional Profile

ABOUT ME

Detail-oriented BIM Architect and Coordinator with 4+ years of experience delivering large-scale residential, commercial, and healthcare developments across Egypt, Saudi Arabia, and the UAE.

Expert in Revit (LOD 350+), Navisworks, BIM 360 / ACC, ISO 19650, OpenBIM (IFC/BCF). Full BIM lifecycle from concept to construction documentation.

Open to remote, hybrid, and part-time engagements. Available GMT+2.

4+

Years

150K+

m² Delivered

30+

Structures

4+

Countries

BIM CORE

- Revit Expert (LOD 350+)
- Navisworks Advanced
- BIM 360 / ACC / CDE
- ISO 19650
- IFC / BCF / OpenBIM
- 4D & 5D BIM

DESIGN

- Interior Design
- Exterior & Facade
- Healthcare BIM
- Master Planning
- Landscape
- 3D Visualization

TECHNICAL

- Shop Drawings
- Municipal Licensing
- BOQ Automation
- As-Built Docs
- Family Creation
- Arc/Str/MEP Coord.

SOFTWARE

- Revit · Navisworks
- AutoCAD · 3ds Max
- Lumion · V-Ray
- BIM 360 · ACC
- Photoshop
- Dynamo

01

BIM

Revit · Navisworks · BIM 360 · ISO 19650 · LOD 350+

Floor Plans

Ground / Typical / Roof levels

Schedules & BOQ

Automated quantity extraction

3D Revit Models

LOD 350+ arch models

Family Creation

Parametric custom families

Exploded Plans

Multi-level axonometrics

Navisworks

Multi-disc. coordination

Sections & Elevations

Technical sections

Clash Detection

Reports & resolution log

Modeling Details

Construction-ready details



CDE & BIM 360

ISO 19650 cloud workflow

Floor Plans & Spatial Layouts

BIM · 01/10 · Revit Architectural Plans


GROUND FLOOR · Scale 1:100

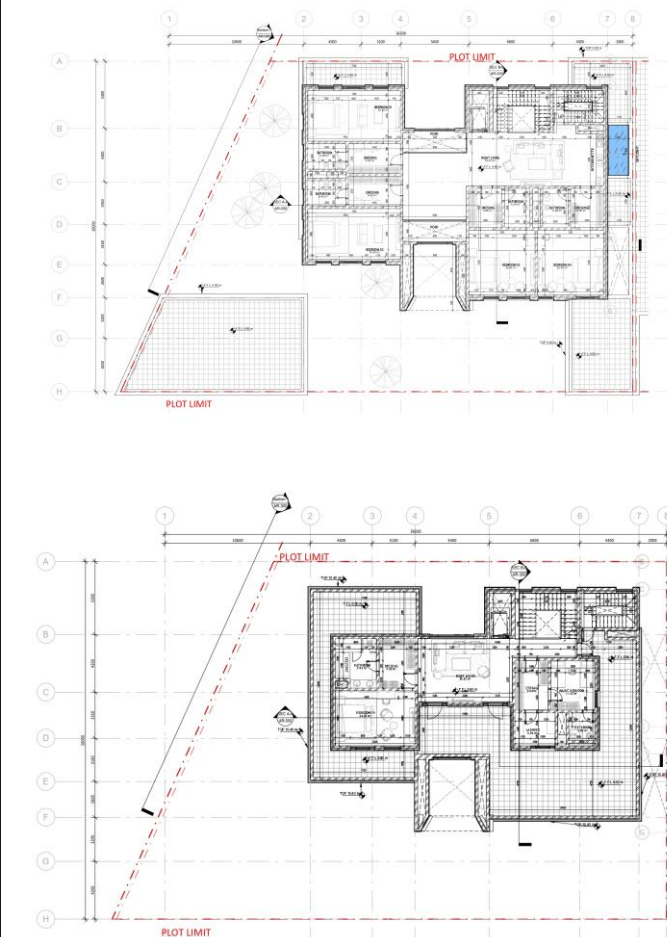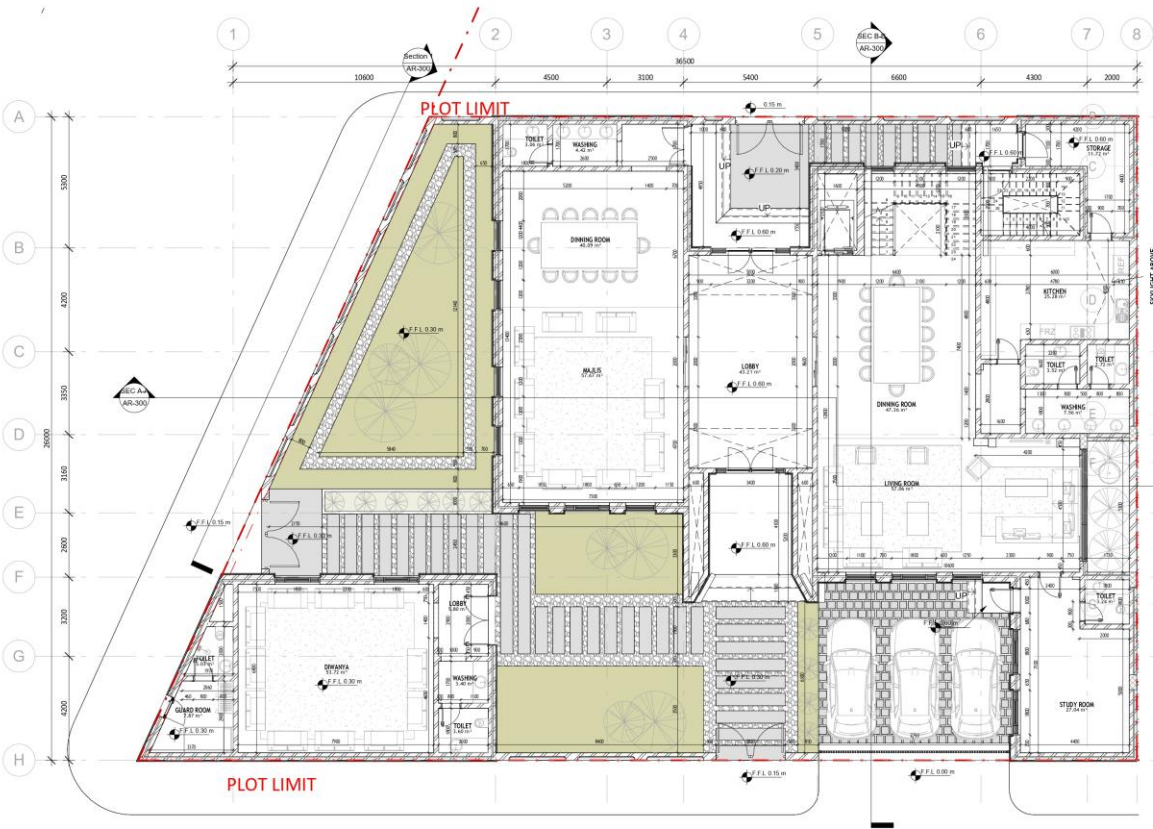

[Project Name] · LOD 350 · Room names · Areas · FFL levels · Door/Window tags


Floor Plans — All Levels

BIM · 01/10 · Complete Plan Set

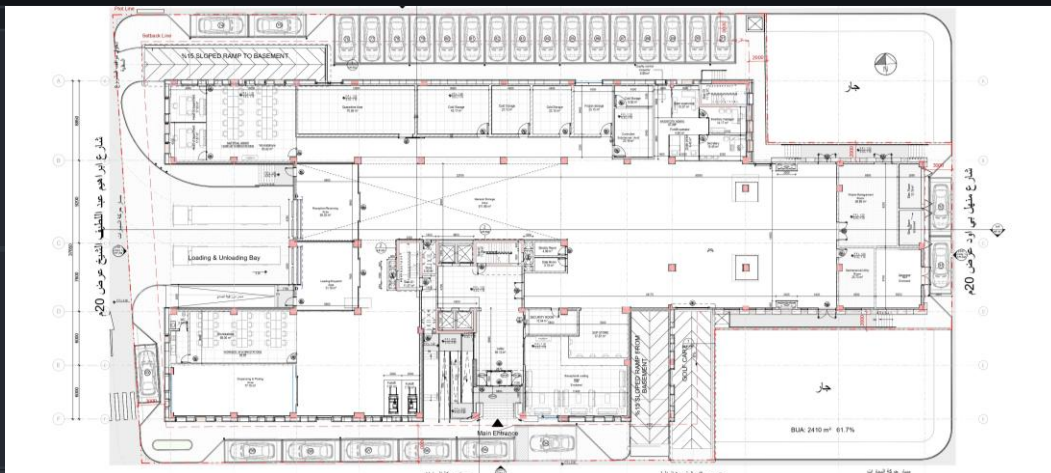

Ground Floor Plan

Sub-ground level

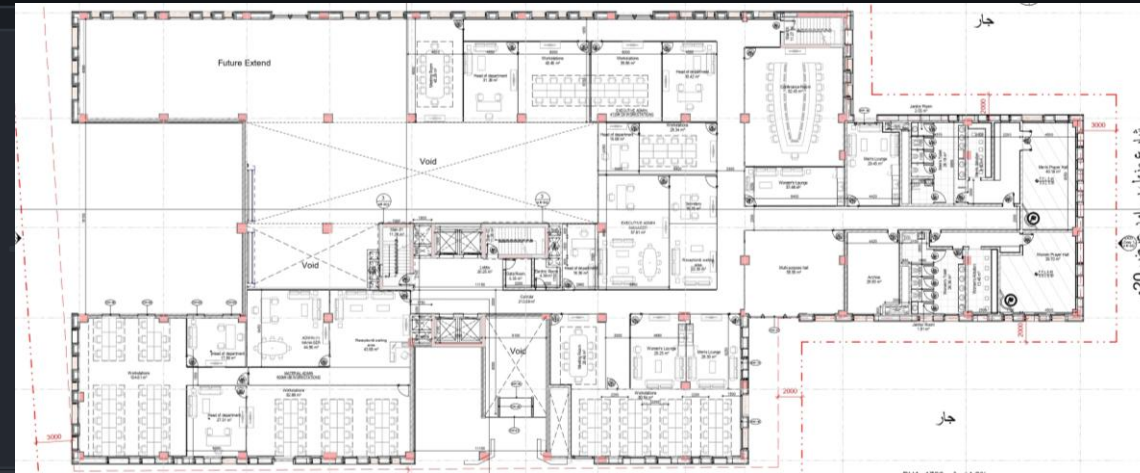

First Floor Plan

Main entrance level



Second Floor Plan

Typical repeating level



Roof Plan

Services & terrace

ELEVATIONS

BIM · 01/10 · Complete ELEVATION Set



WEST ELEVATION

LOADING DOCK



NORTH ELEVATION

SIDE ELEVATION



EAST ELEVATION

SERVICE ELEVATION



SOUTH ELEVATION

MAIN ENTRANCE

3D Revit Models — LOD 350+


BIM · 02/10 · High-Fidelity Architectural Modeling

REVIT 2024



LOD 350+

PARAMETRIC FAMILIES

EXTERIOR 3D VIEW

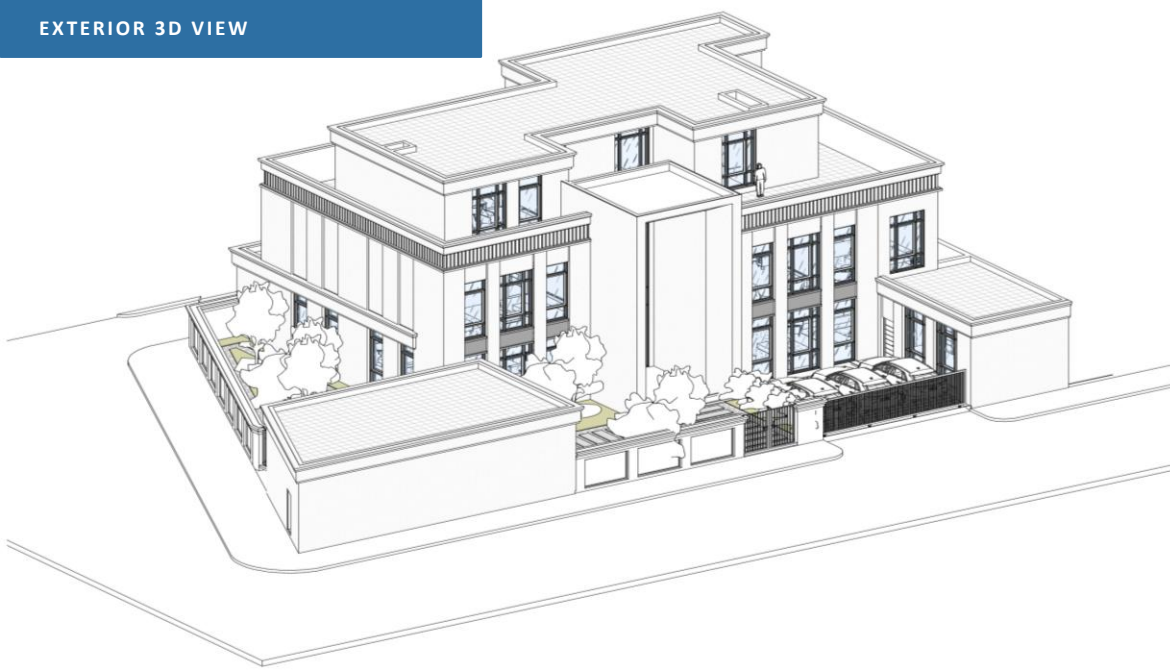


INTERIOR SECTION VIEW

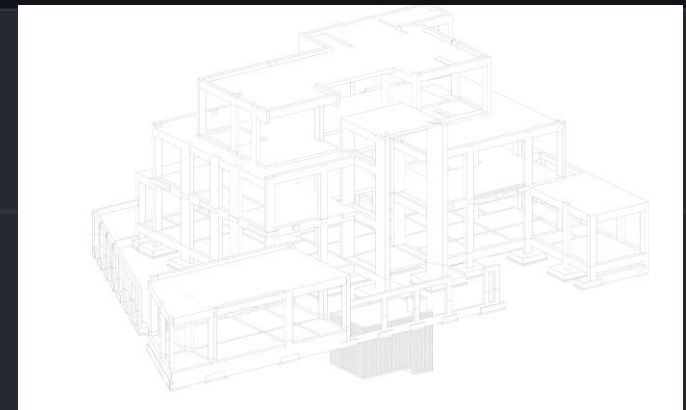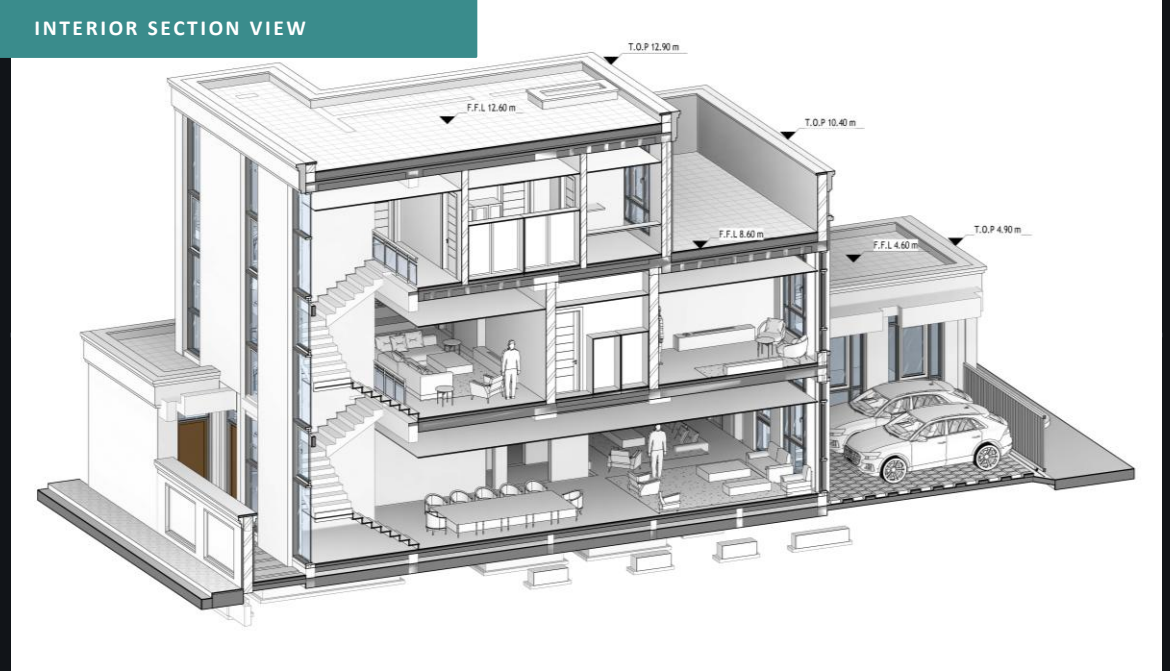

Exploded Axonometric Plans

BIM · 03/10 · Multi-Level Spatial Visualization

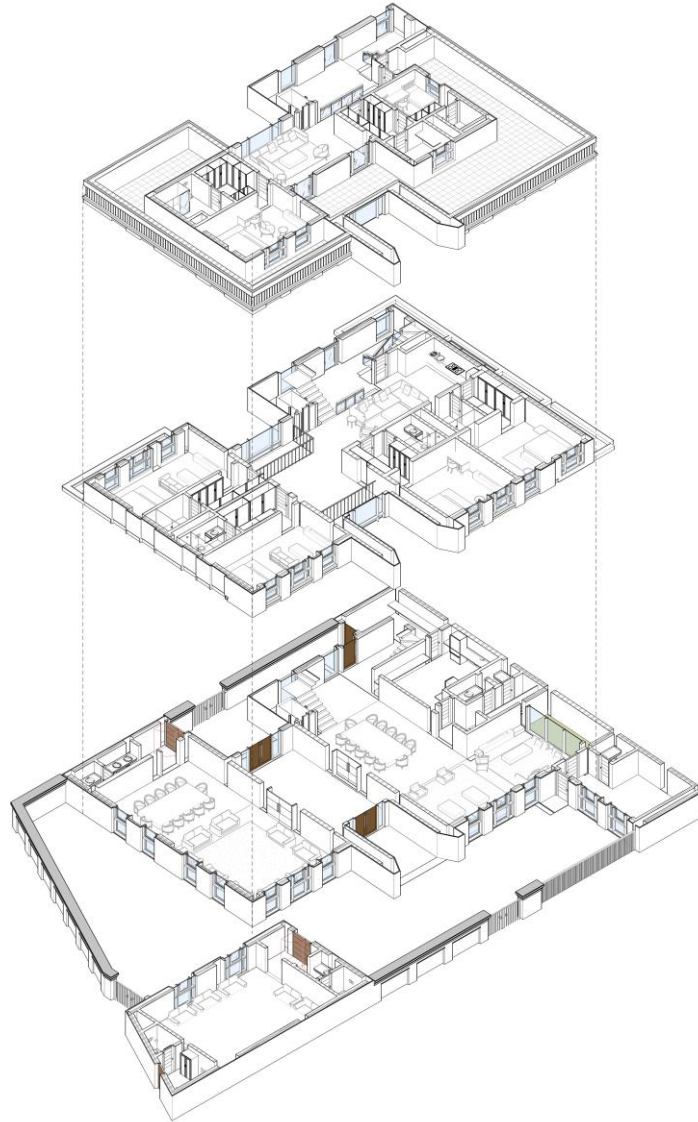

WHAT THIS SHOWS

- Full building disassembled by floor
- Structural slab visibility
- Spatial relationships across levels

The drawing shows a building facade with several levels and heights indicated on the right side:

- +12.6 m ROOF FLOOR
- +8.6 m Penthouse
- +4.6 m First Floor
- +0.6 m GROUND FLOOR
- +0.3 m GARDEN LEVEL
- +0.15 m PAVEMENT LEVEL
- +0 m Base Line

On the left side, there are additional height markers and level indicators:

- T.O.P 11.40m
- T.O.P 10.40m
- T.O.P 4.40m
- T.O.P 2.40m

The drawing also includes various level markers (G1, G2, G3, G4,G99, G100) and a scale bar at the bottom.

The drawing is a detailed architectural elevation of a building facade. It features a central entrance with a large glass door and a prominent vertical window. The facade is divided into several sections with windows of varying sizes and shapes. To the right of the drawing, a vertical scale indicates the following floor levels: +12.6 m ROOF FLOOR, +8.6 m Penthouse, +4.6 m First Floor, +0.6 m GROUND FLOOR, +0.3 m GARDEN LEVEL, +0.15 m PAVEMENT LEVEL, +0 m Base Line, and -0.3 m. The drawing includes various annotations such as 'T.O.F 12.6 m', 'T.O.F 11.4 m', 'T.O.F 10.35 m', and 'T.O.F 4.6 m' indicating the top of floor levels. The building is shown with a flat roof and a series of columns supporting the structure.

Section A-A of the building showing floor levels and room layouts. The section is oriented horizontally, with the ground level on the left and the roof level on the right. The building has three main floors above the ground level, plus a penthouse and a roof floor. The ground floor includes a Hallis (17.67 m²), a Lobby (43.17 m²), a Living Room (17.06 m²), and a Staircase. The first floor includes a Bathroom (5.00 m²), a Dressing (5.94 m²), a Night Living (16.07 m²), and two Bedrooms (Bedroom 03: 15.30 m², Bedroom 04: 16.72 m²). The second floor includes a Bedroom 05 (15.00 m²) and a large open area. The penthouse is located above the second floor. The roof floor is at the top. The section also shows the base line and the ground level. The floor levels are indicated on the right side of the section: +0.6 m (Ground Floor), +0.3 m (Garden Level), +0.15 m (Pavement Level), +0 m (Base Line), +4.6 m (First Floor), +8.6 m (Penthouse), and +12.6 m (Roof Floor). The section also shows the top of the building at +12.6 m. The section is labeled 'SECTION A-A' on the left side.

All 4 with material callouts




Arch & struct 1:50

FFL, room heights

Municipal package

Modeling Details — LOD 350 Precision

BIM · 05/10 · Construction-Ready Technical Details

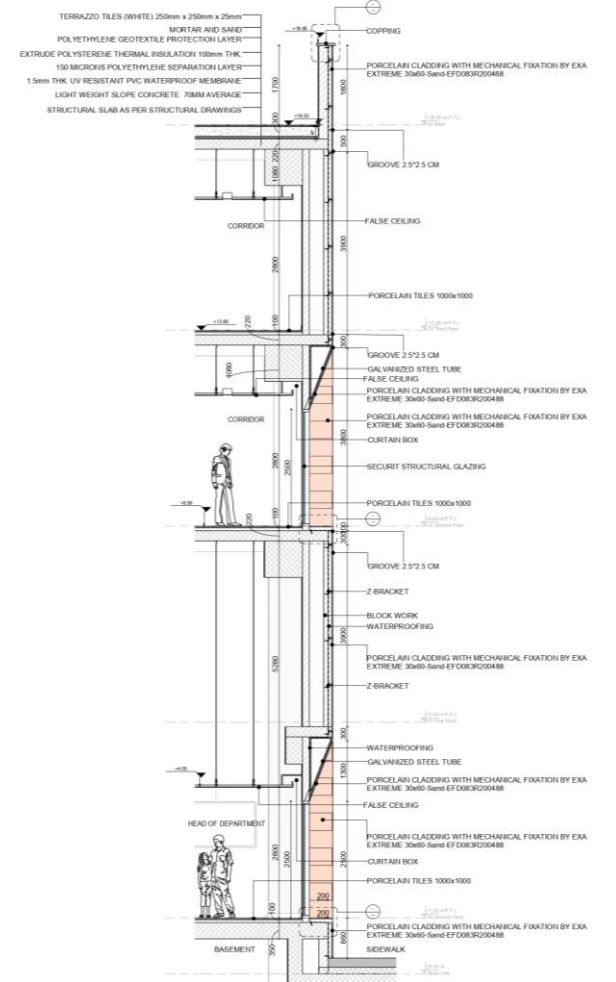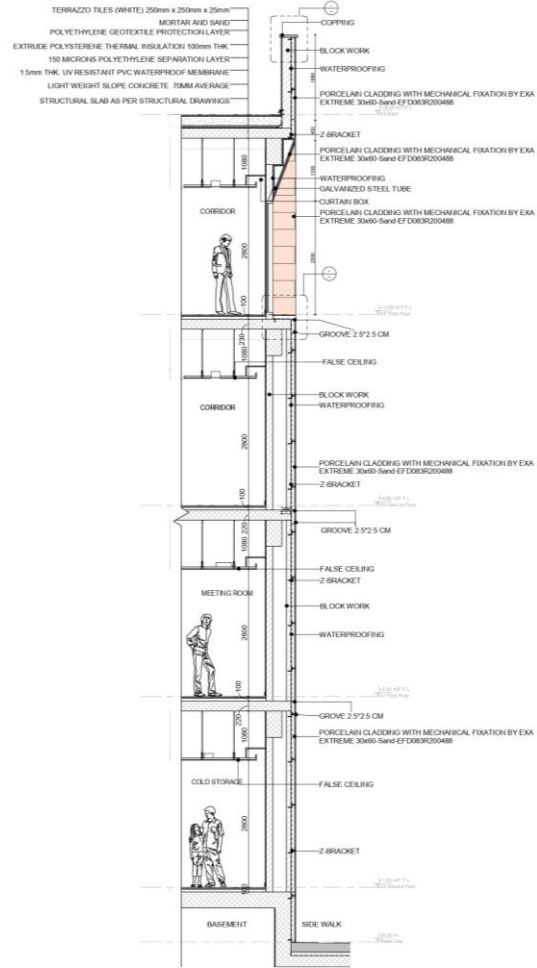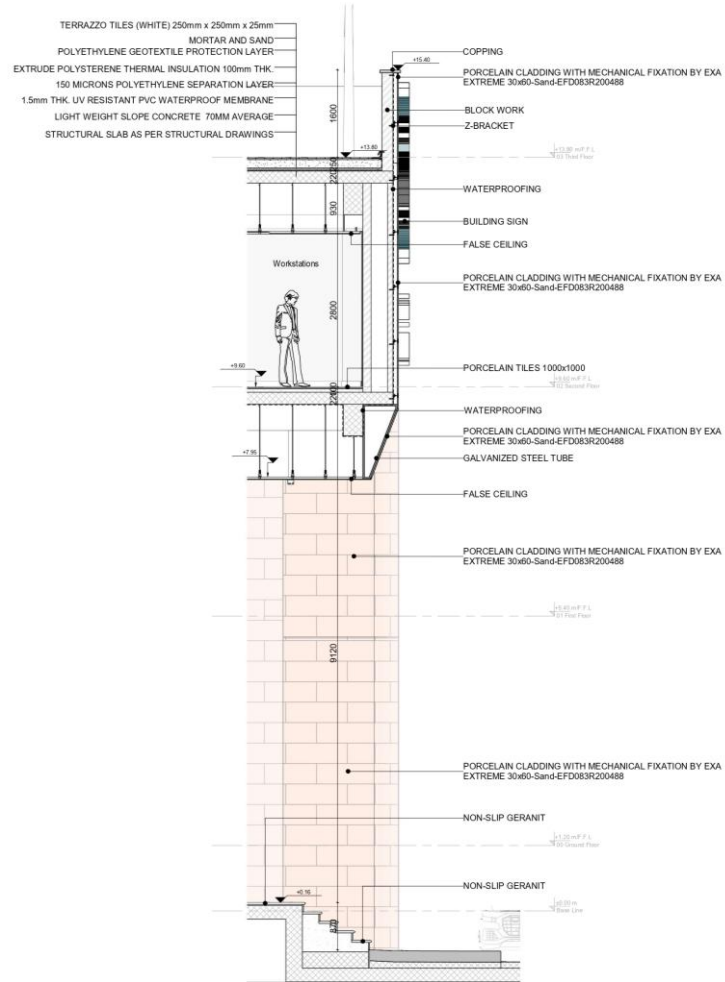

Wall & Facade Details — Deep Dive

BIM · 05/10 · Construction-Ready Specifications

WALL COMPOSITION


External cladding · Z-bracket · Thermal insulation · Blockwork · Internal plaster

FACADE SYSTEM

Curtain wall / unitized panels · Window frame details · Waterproofing layers

KEY STANDARDS

Scale 1:20 · Material specifications · Fire rating notes · Expansion joint details

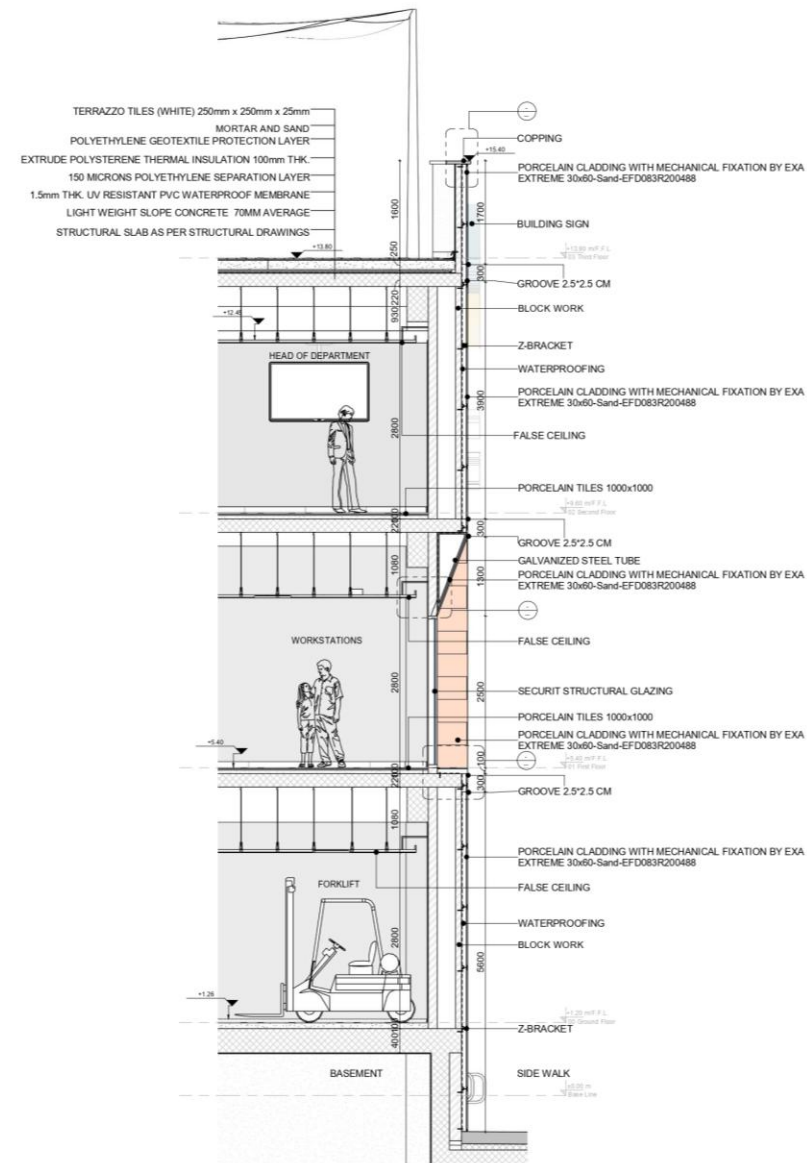

<QD Door Schedule>									
A	B	C	D	E	F	G	H	I	
Family and Type	Type Mat	Phase Created	Description	Count	Rough Width	Rough Height	Area Level	Fire Rating	
#Blandt.com-291-Roller Shutter door: 3950 x 3000	83	Existing		6			GROUND FLOOR		
#Blandt.com-291-Roller Shutter door: 4000 x 2700	80 11	Existing		23			GROUND FLOOR		
#Blandt.com-291-Roller Shutter door: 4000 x 2800	85	Existing		9			GROUND FLOOR		
#Blandt.com-291-Roller Shutter door: 4000 x 3000	80 12	Existing		2			GROUND FLOOR		
#Blandt.com-291-Roller Shutter door: 4100 x 3000	117	Existing		5			GROUND FLOOR		
#Blandt.com-291-Roller Shutter door: 4300 x 2901	96	Existing		3			GROUND FLOOR		
#Blandt.com-291-Roller Shutter door: 4300 x 3200	118	Existing		1			GROUND FLOOR		
#Blandt.com-291-Roller Shutter door: 4700 x 3300	136	Existing		7			GROUND FLOOR		
#Blandt.com-291-Roller Shutter door: 5000 x 3000	43	Existing		1			GROUND FLOOR		
#Blandt.com-291-Roller Shutter door: 5200 x 3000	132	-varies-		4			GROUND FLOOR		
#Blandt.com-291-Roller Shutter door: 6000 x 6000	44	Existing		1			GROUND FLOOR		
#Blandt.com-291-Roller Shutter door: Porta Enroll 100x220	39	Existing		3			GROUND FLOOR		
Chur/Lite Double Door: 2400 x 1500	116	Existing		13			GROUND FLOOR		
Chur/Lite Double Door: 3000 x 2000	119	Existing		1			GROUND FLOOR		
CS Glass Door Double: SAL: 0200 2000/2200	02 01	New Construction		1	800	2200	GROUND FLOOR	DO NOT USE	
CS Glass Door Single: SAL: 0201 1900/2200	02 03	Existing		3	1400	2200	GROUND FLOOR		
CS Metal Door Double Panel with Louvers: AR: SD04 1500X2200	80 04	New Construction	PWR RATED STEEL DOOR DOUBLE LEAVES WITH ANTI-PANIC BAR & FIRE RATED GLASS	1	1500	2200	-varies-		
CS Metal Door Double Panel with Louvers: AR: SD08 1800X2200	80 08	-varies-	PWR RATED STEEL DOOR DOUBLE LEAVES WITH ANTI-PANIC BAR & FIRE RATED GLASS	25	1800	2200	-varies-		
CS Metal Door Double Panel with Louvers: AR: SD09 3000X2300	80 09	-varies-	PWR RATED STEEL DOOR DOUBLE LEAVES WITH ANTI-PANIC BAR & FIRE RATED GLASS	13	3000	2300	-varies-		
CS Metal Door Double Panel with Louvers: AR: SD15 4000X3000	80 10	New Construction	PWR RATED STEEL DOOR DOUBLE LEAVES WITH ANTI-PANIC BAR & FIRE RATED GLASS	2	4000	3000	GROUND FLOOR	1 H	
CS Metal Door Double Panel with Louvers: SAL: SD01 2400X2200	80 01	New Construction	PWR RATED STEEL DOOR DOUBLE LEAVES WITH ANTI-PANIC BAR & FIRE RATED GLASS	1	2400	2200	SPL. SERVICE		
CS Metal Door Single Panel: SAL: SD02 1000X2200H	80 02	New Construction	PWR RATED STEEL DOOR SINGLE LEAF WITH WOODEN TEXTURE	14	1000	2200	MEZZ FLOOR	1H	
CS Metal Door Single Panel: AR: SD01 1000X2200	80 01	-varies-		114	1000	2200	GROUND FLOOR		
CS Metal Door Single Panel: SAL: SD06 1000X2200H-std	80 06	New Construction		1	1000	2200	T-CAMIN	1 H	
CS Metal Door Single Panel: SAL: SD08 1000X2200	80 08	New Construction		1	1000	2200	T-CIP 1 FLOOR		
CS Wooden Door Single Panel: SAL: WD01 1900X2200	WD 01	-varies-	WOODEN DOOR SINGLE LEAF (ANDER CUT)	15	740	2200	GROUND FLOOR		
CS Wooden Door Single Panel: SAL: WD02 1800X2200	WD 02	-varies-	WOODEN DOOR SINGLE LEAF (ANDER CUT)	5	840	2200	-varies-		
CS Wooden Door Single Panel: SAL: WD03 1600X2200: PWR 45MIN	WD 03	New Construction	STEEL DOOR SINGLE LEAF (ANDER CUT)	2	1500	2200	MEZZ FLOOR	45	
CS Wooden Door Single Panel: SAL: WD03 1800X2200	WD 03	-varies-	WOODEN DOOR SINGLE LEAF (ANDER CUT)	98	980	2200	-varies-		
CS Wooden Door Single Panel: SAL: WD04 3000X2200	WD 04	New Construction	WOODEN DOOR SINGLE LEAF (ANDER CUT)	1	3400	2200	MEZZ FLOOR		
Door&Ls: 1400 x 1700 mm 4	107	Existing		1			GROUND FLOOR		
Door&Ls: 1700 x 1700 mm 3	105	Existing		1			GROUND FLOOR		
Door&Ls: 1700 x 2700	153	New Construction		1			MEZZ FLOOR		
Door&B&E: Pate: P3PM 1037X 650 x 2100	73	Existing		1	670	2135	GROUND FLOOR		

<QS Window Schedule>					
A	B	C	D	E	
Family and Type	Description	Count	Rough Width	Rough Height	
Awning Casement: 1000 x 1000		35			
Awning Casement: 1000 x 1600		6			
Awning Casement: 1000/1200		2			


Area Schedule

GFA · NFA · room-by-room


Shop Drawing Modeling






Exterior Façade

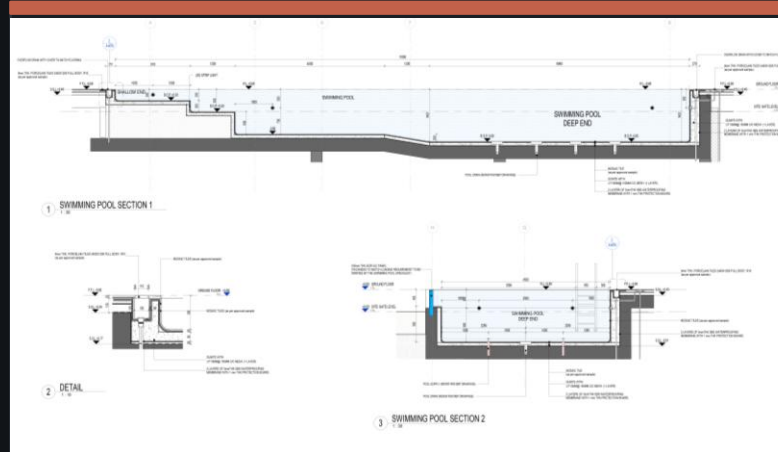

Private swimming Pool

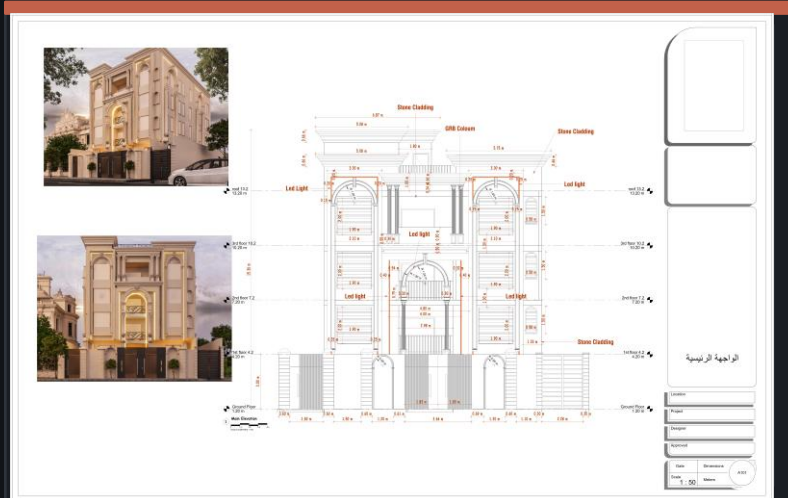


Exterior Façade

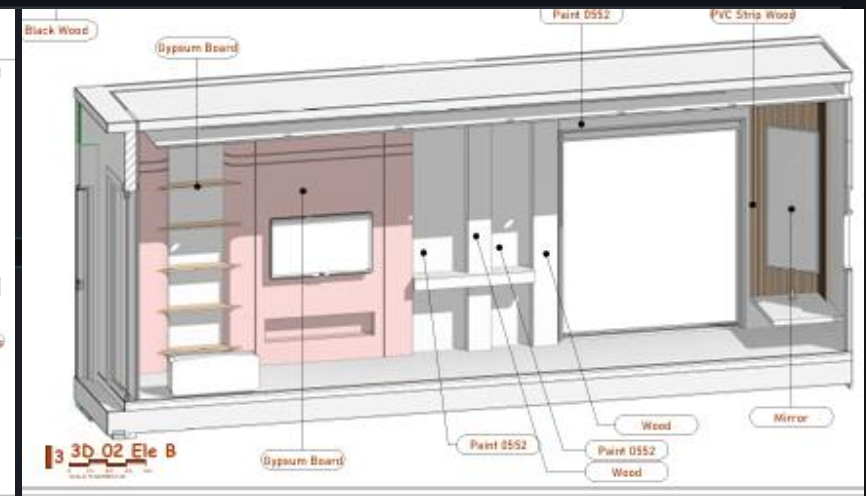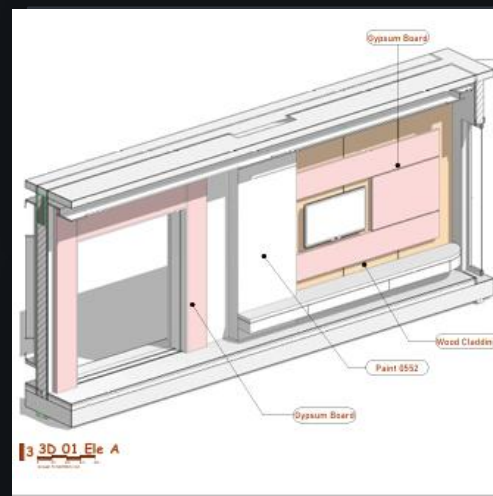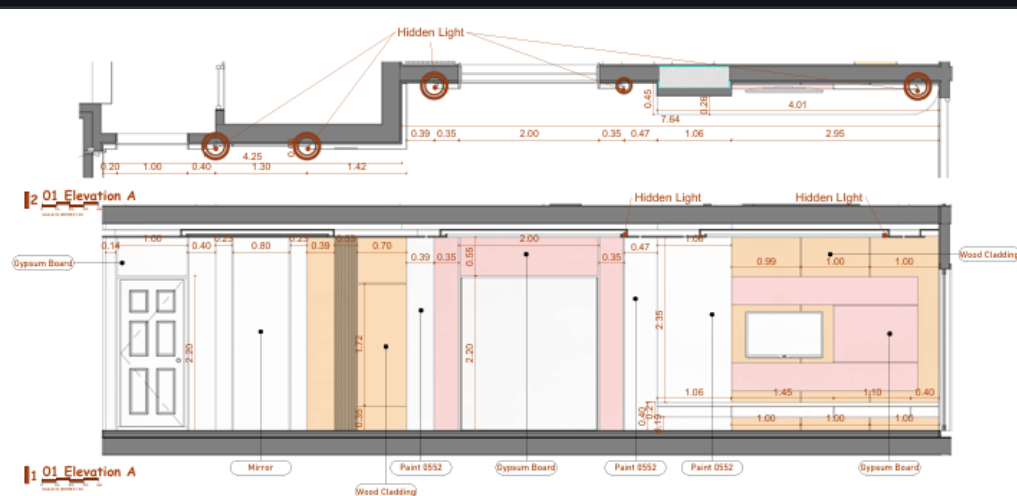

Navisworks Multi-Disciplinary Coordination

BIM · 08/10 · Arc + Str + MEP Federated Model

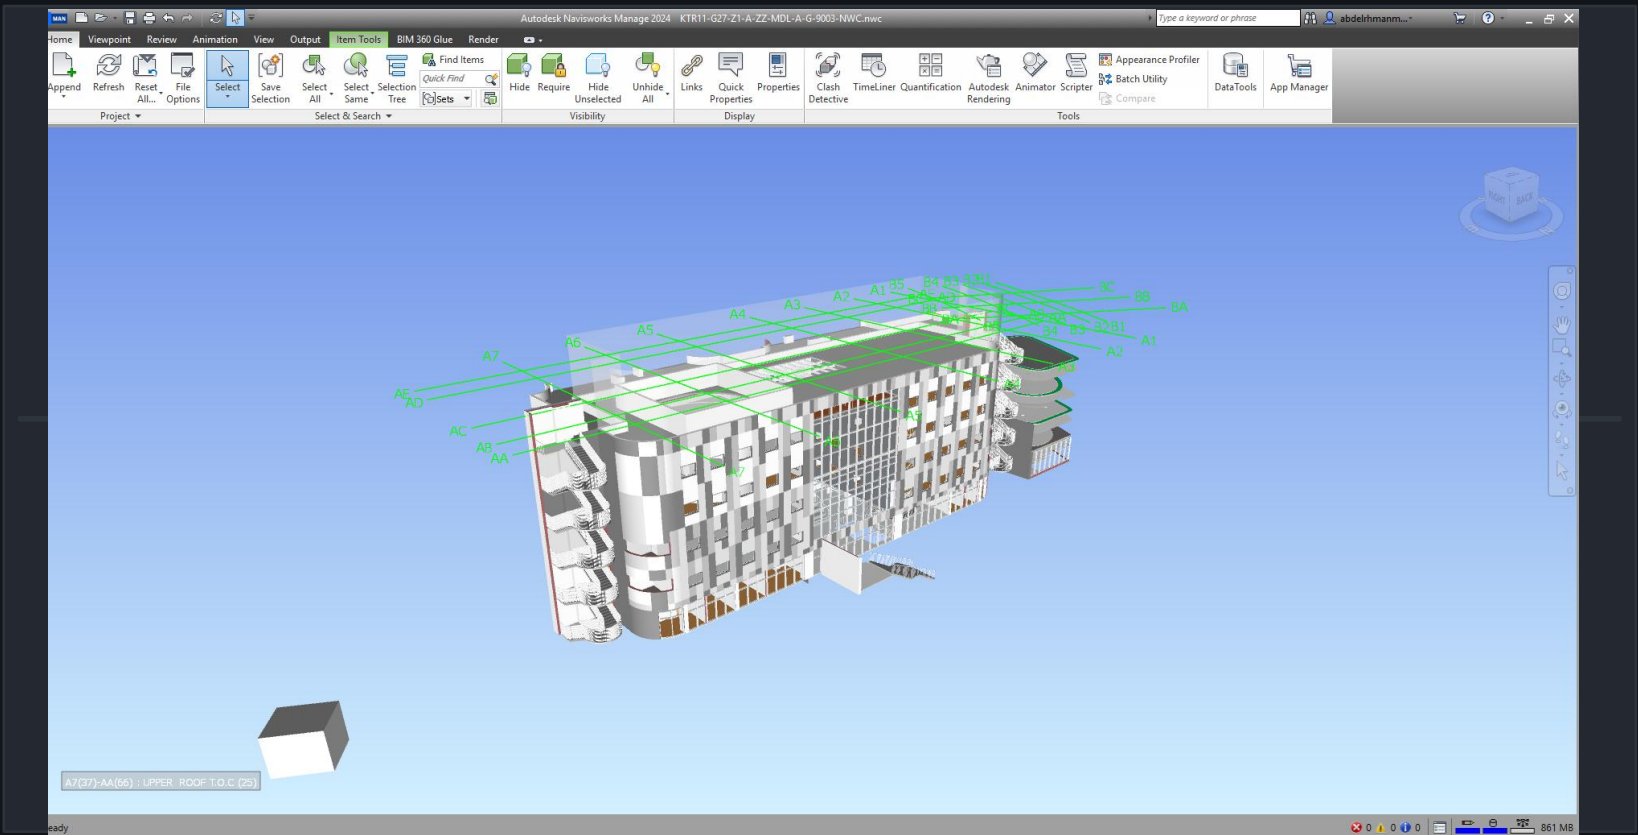

DISCIPLINES

Architectural · Structural
MEP (Mech + Elec + Plumbing)

WORKFLOW

NWC export → Append → Clash tests → Issue log → Resolution

OUTPUTS

Clash Report · Issue Log · Resolution Register

STEP 1 — Aggregation

NWC export per discipline → Navisworks append → Federated model

STEP 2 — Clash Testing

Run Clash Detective → Hard & soft clashes → Filter by discipline

STEP 3 — Resolution

Issue → Assign → Model fix → Re-run → Zero-clash sign-off

Clash Detection — Reports & Resolution

BIM · 09/10 · Zero Conflicts Before Construction

Clash Detective

AR Stairs-vs-MEF Pipe& Fittings

Last Run: Sunday, February 9, 2025 10:03:24 PM

Clashes - Total: 9 (Open: 0 Closed: 9)

Name	Status	Clashes	New	Active	Reviewed	Approved
AR Stairs-vs-EL Security Devices	Done	2	0	0	0	0
AR Stairs-vs-MEF Pipe& Fittings	Done	9	0	0	0	0
AR Stairs-vs-MEF Sprinklers	Done	2	0	0	0	0
AR Stairs-vs-MEH Air Terminals	Done	2	0	0	0	0

Add Test

Reset All

Compact All

Delete All

Update All

Rules

Select

Results

Report

Contents

☒ Summary

☐ Clash Point

☒ Date Found

☐ Assigned To

☐ Date Approved

☐ Approved By

☐ Layer Name

☐ Item Path

☒ Item ID

Include Clashes

For Clash Groups, include:

Everything

☒ Include only filtered results

Include these statuses:

☒ Active

☒ Reviewed

☒ Approved

☒ Resolved

Output Settings

Report Type

All tests (combined)

Report Format

HTML (Tabular)

☒ Preserve result highlighting

Write Report

9

Clashes Found

100%

Resolved

3

Disciplines

RESOLUTION WORKFLOW


Detect → Tag → Assign discipline → Coordination meeting → Model correction → Re-run test → Mark resolved → Update report → Final zero-clash sign-off

ABDELRHMAN MOHSEN · BIM Architect & Coordinator



BIM — Clash

Clash Detection — Reports & Resolution


BIM · 09/10 · Zero Conflicts Before Construction

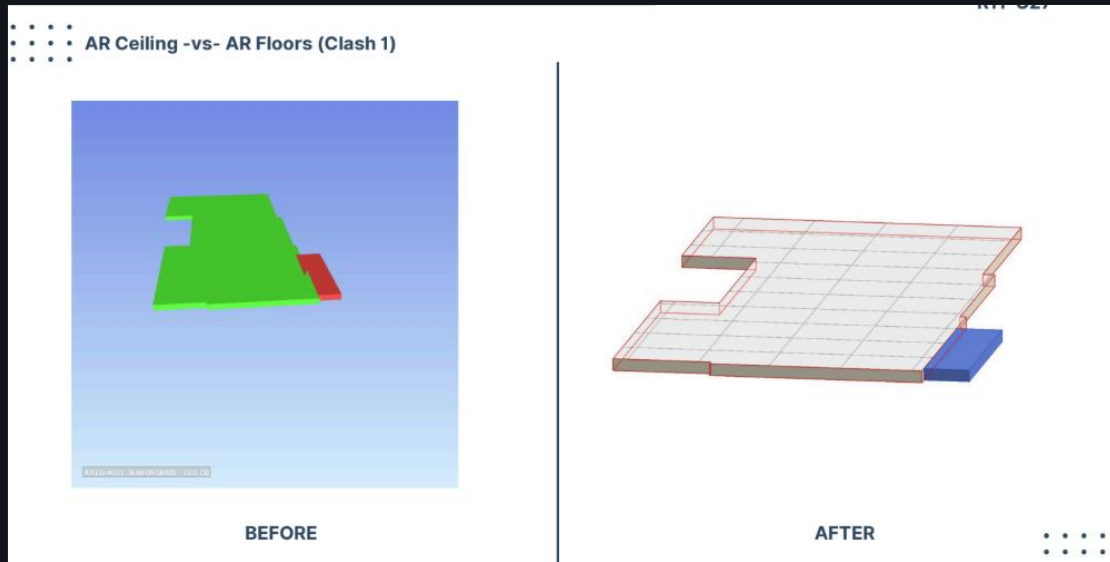

BEFORE — Active Clashes Detected

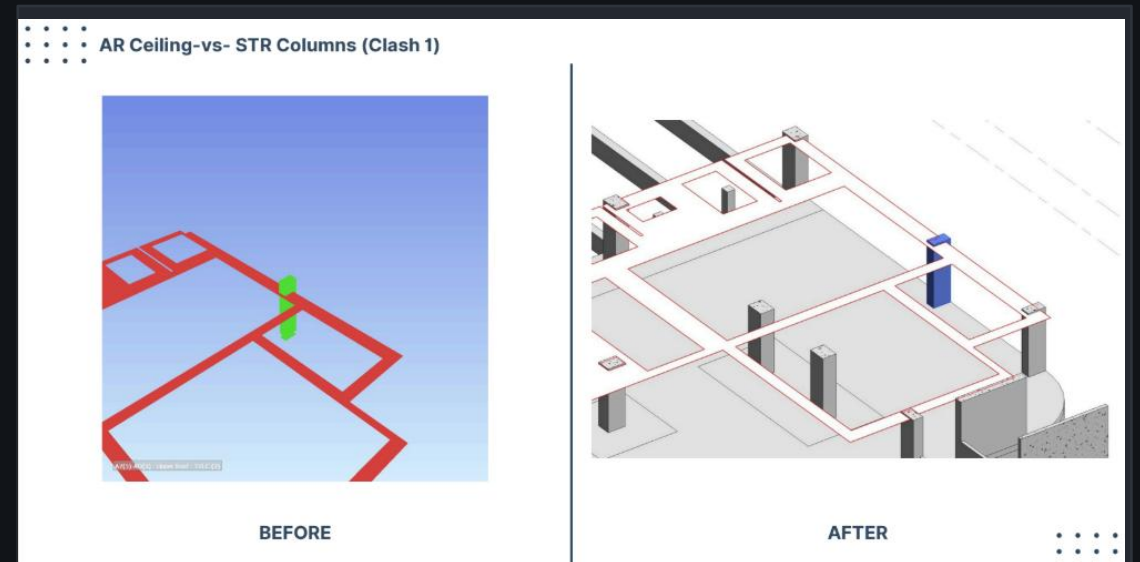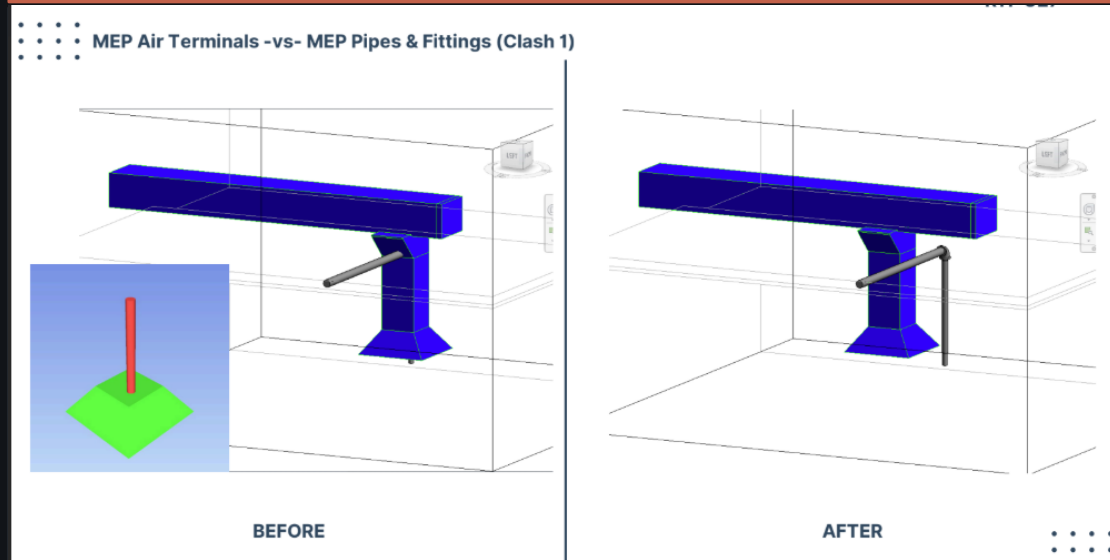


BEFORE — Active Clashes Detected

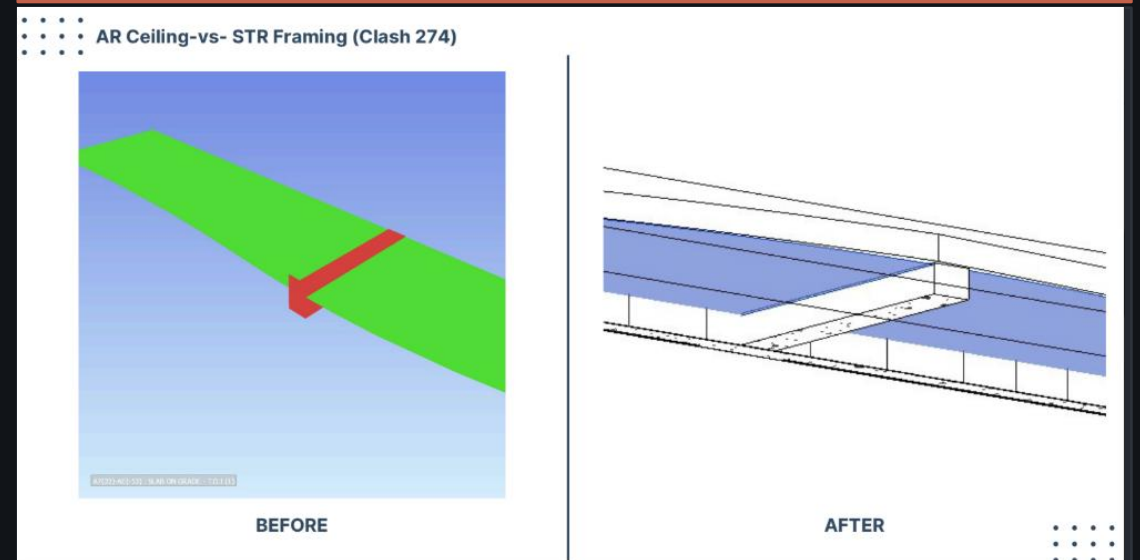


Clash Detection — Reports & Resolution

BIM · 09/10 · Zero Conflicts Before Construction

AR Curtain Walls-vs- EL Communication Devices (Clash 73)

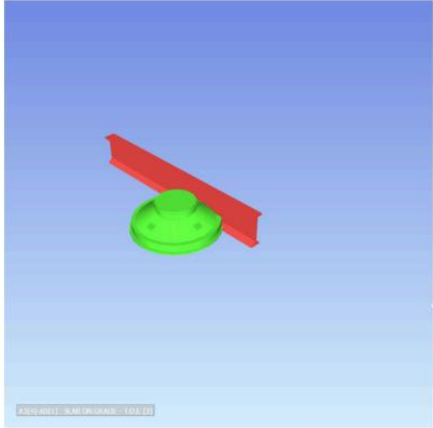


BEFORE

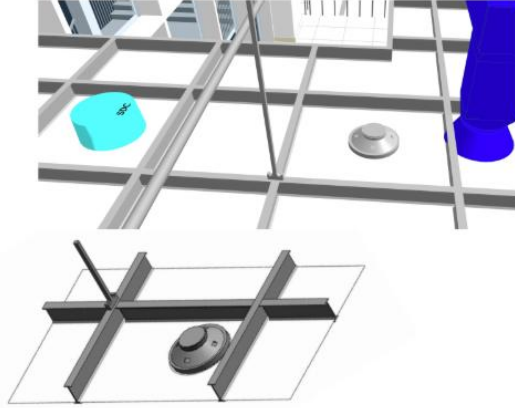


AFTER

BEFORE — Active Clashes Detected

MEP Sprinklers -vs- EL Fire Alarm (Clash 1)

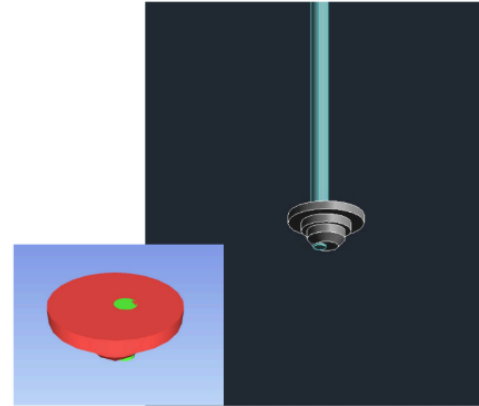


BEFORE

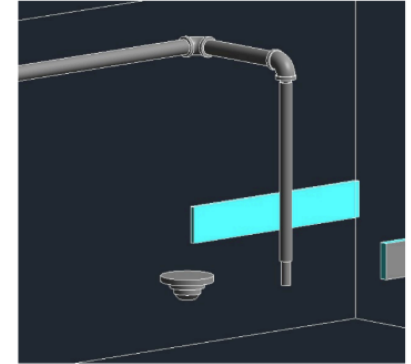


AFTER

BEFORE — Active Clashes Detected

STR Columns -vs- MEP Pipes&Fittings (Clash 2)

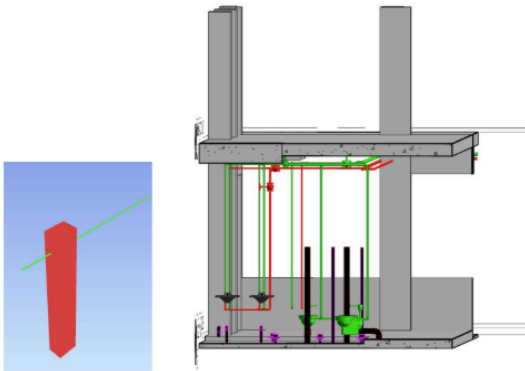


BEFORE

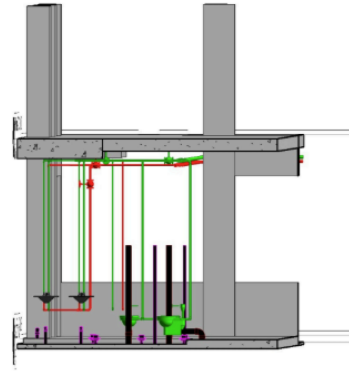


AFTER

AR Curtain Walls Mullions-vs- EL Lighting Equipments (Clash 13)

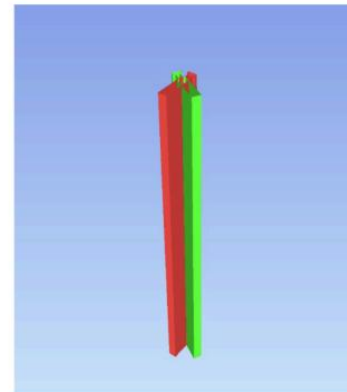

BEFORE

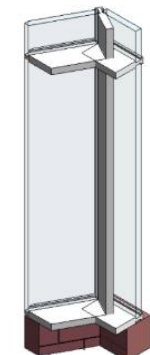

AFTER

Common Data Environment — BIM 360 / ACC

BIM · 10/10 · ISO 19650 Cloud Collaboration

Folder Structure

Files

Folders Packages

Project Files

01-WIP

02-Shared

03-Published

04-Archived

05-Coordination

06-Incoming

07-Bim Library

08-Resources

Files

Folders Packages

Project Files

01-WIP

02-Shared

03-Models

03-Shared Level/Model

03-Structure

03-Mechanical

03-Sheets

03-BIM

03-Architecture

03-Structure

03-Mechanical

03-Electrical

Files

Folders Packages

Project Files

01-WIP

02-Shared

03-Models

03-Structure

03-Mechanical

03-Sheets

03-BIM

03-Architecture

03-Structure

03-Mechanical

03-Electrical

Permissions

26 days remaining on 2 of your trials [View buying options](#)

Permissions

Project Files

Users: 26 Companies: 1 Roles: 1

+ Add

Search for name or email

You're viewing data with filters/sorting applied. [Clear all](#)

Name	Permissions	Type
mostafa kamal	Edit	User Remove
mustafa mohammed	Edit	User Remove
Nada Mohamed	Edit	User Remove
Nayera Kamel	Edit	User Remove
Soliman Elid	Edit	User Remove
Yasmeen Ali	Edit	User Remove
Younna Bahaa	Edit	User Remove

Add Members

27 days remaining on 2 of your trials [View buying options](#)

Add Members

Members

+ Add members

Export Search members by name or email...

Name	Email	Phone	Status	Company	Role	Access level	Added on	Docs	Design Collaboration
Yasmeen Ali	yasmeenali27...	2...	Active	Kaltech	Architect	Project member	01/03/2025		
Abdelrahman Tarek	eng.abdelrah...	-	Active	Kaltech	Architect	Project member	01/03/2025		
Ahmed Saeed	ahmedsaeed1...	5...	Active	Kaltech	Structure Engineer	Project member	01/03/2025		
Ahmed Sayed	ashkhatib0...	2...	Active	Kaltech	Mechanical Engineer	Project member	01/03/2025		
Younna Bahaa	younna.kalle...	-	Active	Kaltech	Architect	Project member	01/03/2025		
Nayera Kamel	nayera.kamel...	2...	Active	Kaltech	Architect	Project member	01/03/2025		
Hazem Sakr	hazem.sakr...	-	Active	Kaltech	Architect	Project member	01/03/2025		
Ahmed Masoud	ahmedmasoud...	2...	Active	Kaltech	Mechanical Engineer	Project member	01/03/2025		
Osama Elshafey	asad1703@q...	-	Active	Kaltech	Mechanical Engineer	Project member	01/08/2025		
mostafa kamal	mostafakamal...	2...	Active	Kaltech	Structure Engineer	Project member	01/08/2025		
mahmoudmansour4799...	mahmoudman...	-	Invited	Kaltech		Project member	01/08/2025		

ISO 19650 Compliance

Structured delivery per ISO 19650-2

Document Management

WIP→Shared→Published→Archive
Revision control

Model Coordination


Federated model viewing
Issue tracking & BCF

RFI & Issues

Cloud-based issue log
Linked to 3D objects


6D—Sustainability and Lifecycle Management

MICRO CLIMATE

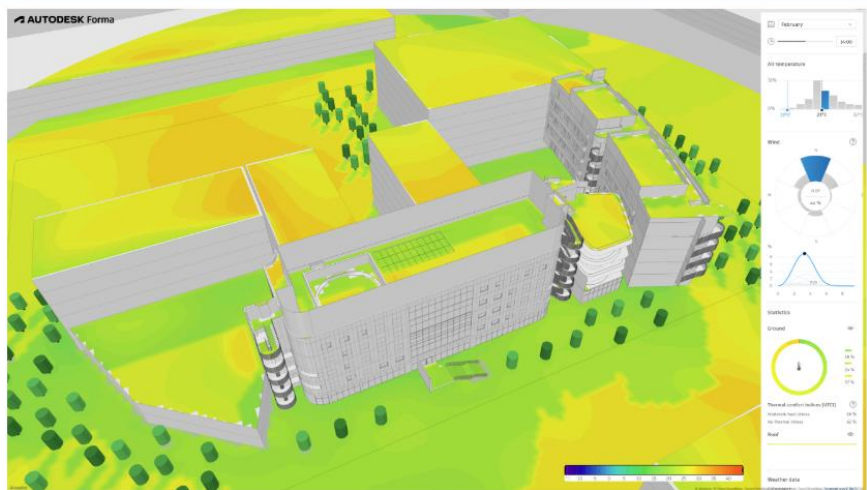


SOLAR ENERGY


CURRENT CASE

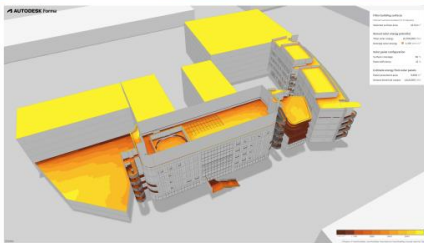

PROPOSED CASE

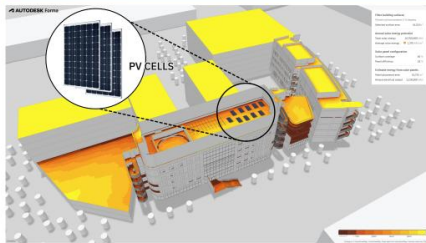

CONCLUSION

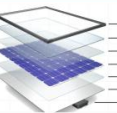


Installing solar panels on the school rooftops is a sustainable architectural solution that enhances the educational environment in several ways:


- 1-Sustainability and Energy Efficiency: Reduces dependence on traditional energy sources, contributing to lower fossil fuel consumption.
- 2-Improved Learning Environment: Helps reduce carbon emissions, improving indoor air quality & Lowers rooftop temperatures by providing shade, reducing the building's thermal load.
- 3-Reduced Operational Costs: Lowers electricity bills, allowing funds to be allocated to educational facility improvements and enables surplus electricity to be sold to the power grid, generating additional financial returns.

DAYLIGHT POTENTIAL

CURRENT CASE

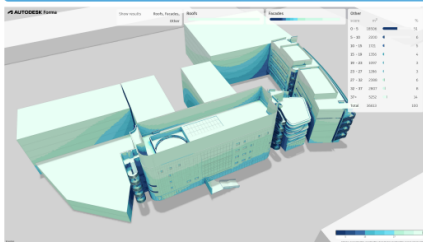


PROPOSED CASE

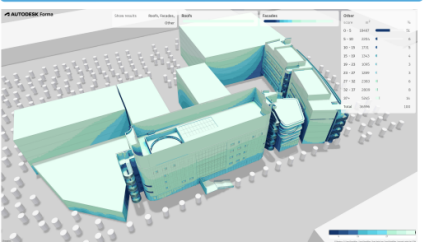


CONCLUSION

1. Skylights or roof monitors: adding skylights or clerestory glazing can provide consistent overhead light.
2. Increase window area in critical zones: Enlarging windows or adding glazing can improve daylight.
3. Consider window placement and sill heights: Higher window heads can allow deeper daylight penetration into interior spaces.
4. Landscape design: Strategic tree placement can control glare and heat gain without excessively blocking daylight.

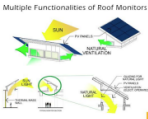

WIND

CURRENT CASE

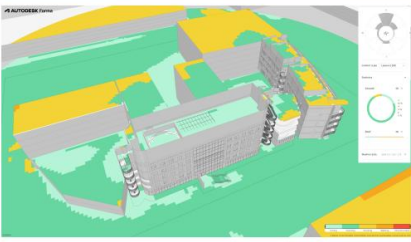

PROPOSED CASE




CONCLUSION

- 1- Adding windbreak fences of vegetation around outdoor spaces.
- 2-Using perforated panels to break down strong wind impacts.
- 3-Using double glass in facades to buffer wind pressure.



SUN HOURS

CURRENT CASE

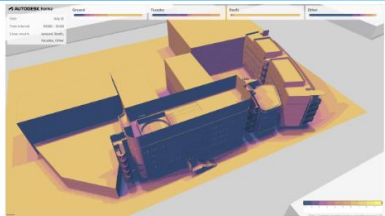

PROPOSED CASE



CONCLUSION


1. Shading Devices & Architectural Elements

- Movable or fixed louvers made of sustainable materials to control sunlight
- Green Facades reduce heat gain and provide natural cooling




2. Passive Design Strategies

- Proper building orientation, courtyards, double-skin facades, and earth-sheltered designs optimize cooling

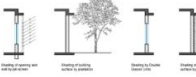


3. High-Performance Materials

- Reflective roofs, Low-E glass, solar films, and phase change materials minimize heat gain.

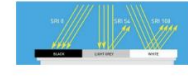


EMBODIED CARBON

CURRENT CASE

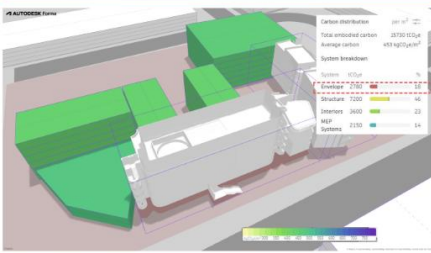

PROPOSED CASE

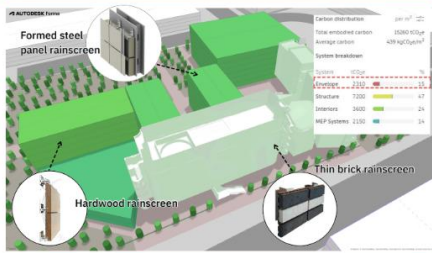


CONCLUSION

Using low-carbon materials, such as low-emission concrete, recycled timber, steel & brick rainscreen cladding helps reduce the carbon footprint to 3% at least:


- 1- Brick rainscreen (18mm) thin brick bonded with type S mortar on a galvanized steel backing tray, hung on a galvanized steel support system and thermally broken from the wall framing.
- 2- Formed Steel Panel Rainscreen: 22 gauge (<1mm) painted roll-formed steel panel hung on a galvanized steel support system and thermally broken from the wall framing.
- 3- Hardwood Rainscreen: 1" (25mm) fast-growing domestic hardwood with a water-based finish hung on a galvanized steel support system and thermally broken from the wall framing.

NOISE

CURRENT CASE

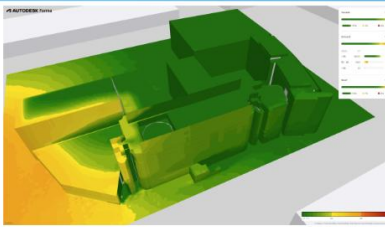

PROPOSED CASE

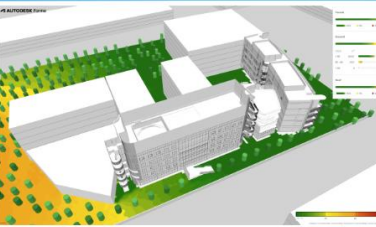


CONCLUSION


1. Use soundproof windows & doors: Double or triple glazing with airtight seals. Larger air gaps between glass panes absorb more noise.
2. Install sound barriers: Green walls, fences, or earth mounds to block road noise. Trees, shrubs, and vertical gardens absorb and scatter sound.
3. Seal gaps and cracks: Use weather stripping and acoustic caulking around windows and doors.




Shadow Study

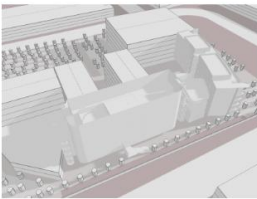


08-00am, 21th of July

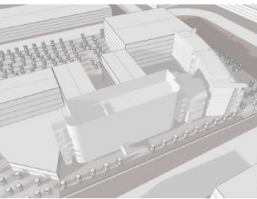


10-00am, 21th of July

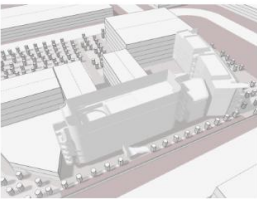


12-00pm, 21th of July

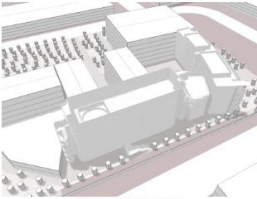

02-00pm, 21th of July

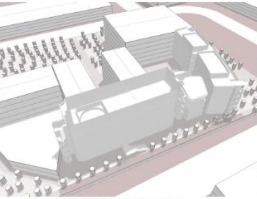

04-00pm, 21th of July

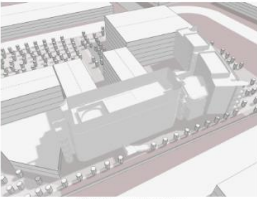

06-00pm, 21th of July

02

EXTERIOR & LANDSCAPE

Facades · Villas · Compounds · Master Plans · Pool Areas · Garden Design



EXTERIOR & FACADE DESIGN

[SQURAE BUSNISSH HUB] · [NEW DAMIETTA] · [10000 m²] · [2025]

Exterior Design — Contemporary Collection



Villa 108 — Contemporary

Modern · SAUDI ARABIA



Compound Unit — Clean Facade

Residential · Egypt



Mixed-Use Building

Residential + Residential

Exterior Design — Classical Villas

MAIN HERO · 3D Render



[M3MAR VILLA] · Classical Style · [QATAR] · [600 m²]

Exterior & Landscape

Exterior Design — Project Collection

EXTERIOR · 03/05 · Selected Works



Villa — Classical

[QATAR · 800m²]



Villa — Contemporary

[QATAR · 400 m²]



ESTRA7A

[SAUDI · 350m²]



Commercial Facade

[NEW DAMITTA · m²]



ESTRA7A

[SAUDI · 350m²]



Commercial Facade


[NEW DAMITTA · m²]

Exterior Design — RESIDENTIAL

RESIDENTIAL · Street Level View



ESTRA7A · LANDCAPE

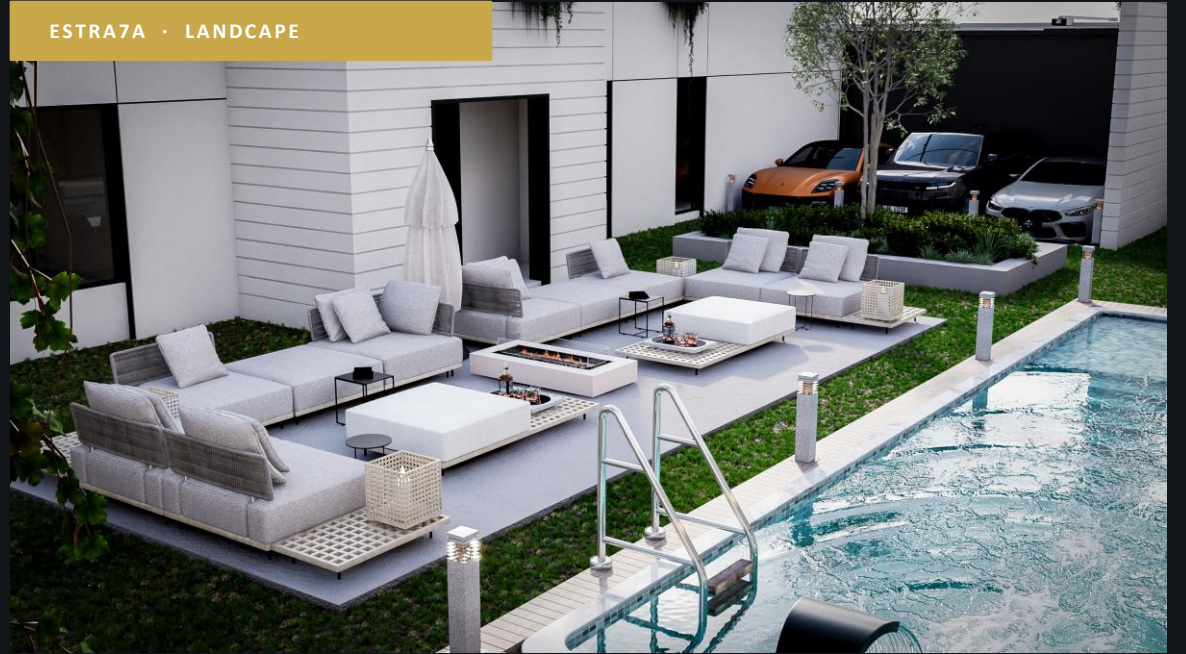

Exterior Design — Project Collection



BUILDING — Classical

[CAIRO · 400m²]



Villa — GARDEN

[SAUDI · 50m²]



Villa — GARDEN

[SAUDI · 50m²]



Villa — GARDEN

[SAUDI · 350m²]



Master Plan Aerial

[EGYPT · 50000m²]



MALL

[NEW DAMIETTA · 400m²]

03

INTERIOR DESIGN

Luxury Residential · Hospitality · Contemporary



ABDEL RHMAN MOHSEN

INTERIOR DESIGN · LUXURY RESIDENTIAL

[YASSER VILLA · SAUDI · MODERN]

ABDEL RHMAN MOHSEN · BIM Architect & Coordinator

Interior Design

Interior Design — Living Spaces




LIVING-ROOM· Contemporary Luxury



MAJLIS· CLOSE Plan Design

Interior Design — Dining & Kitchen

DINING ROOM · Hero View

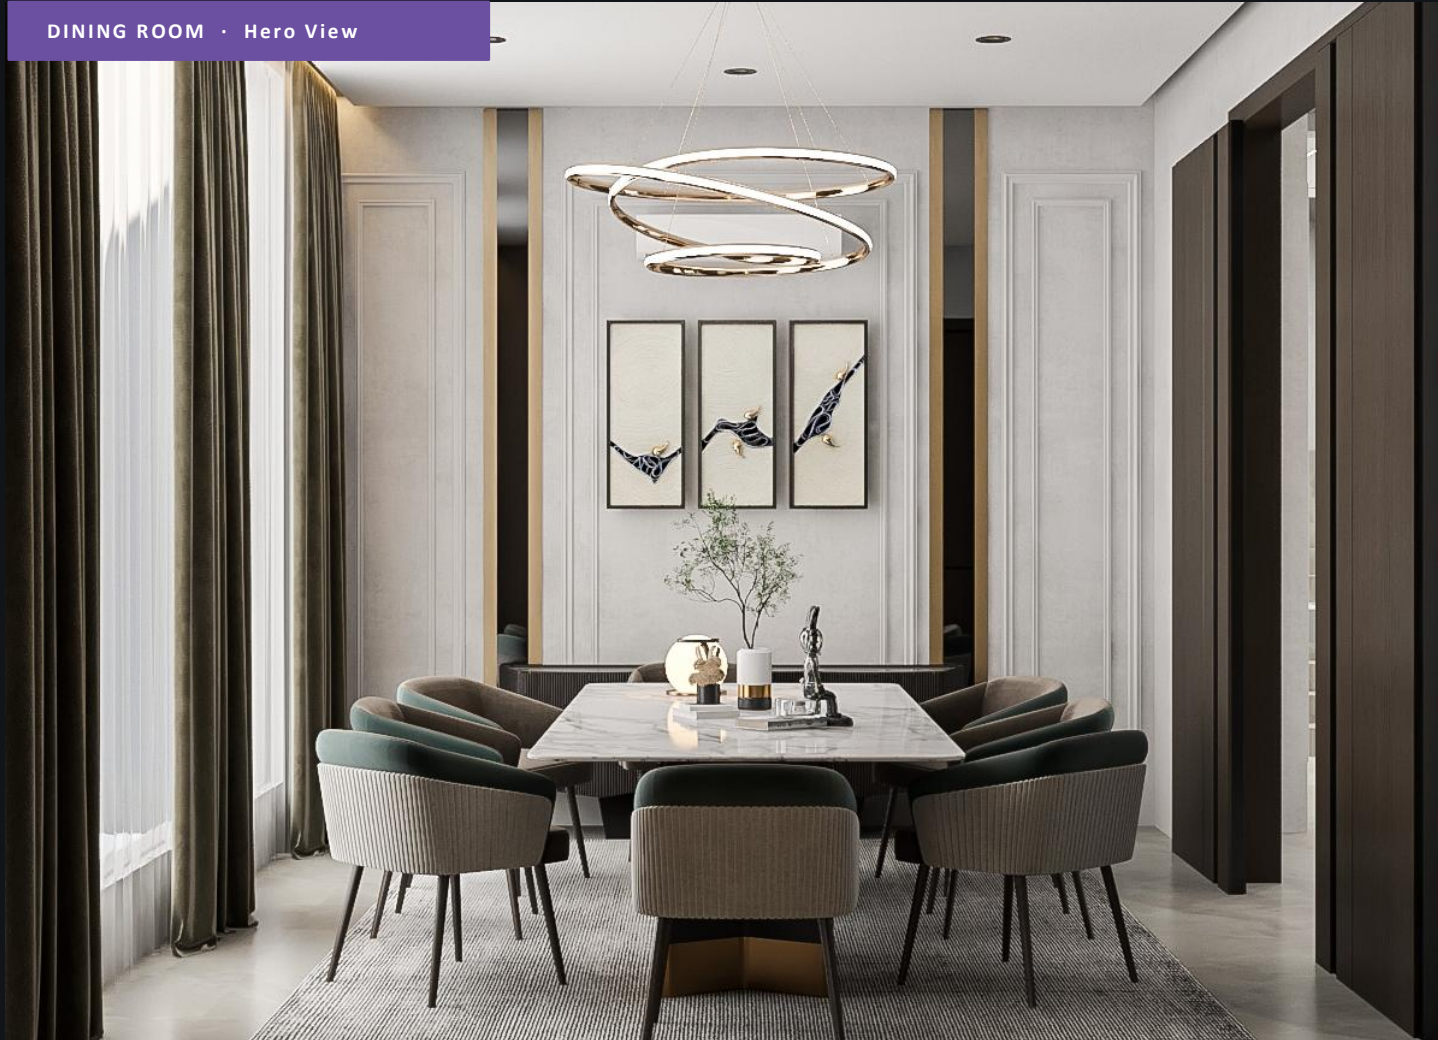

[SARA] · Dining · [NEO CLASSIC]




Interior Design — Bedroom Collection



Luxury Master Suite

Contemporary minimalist

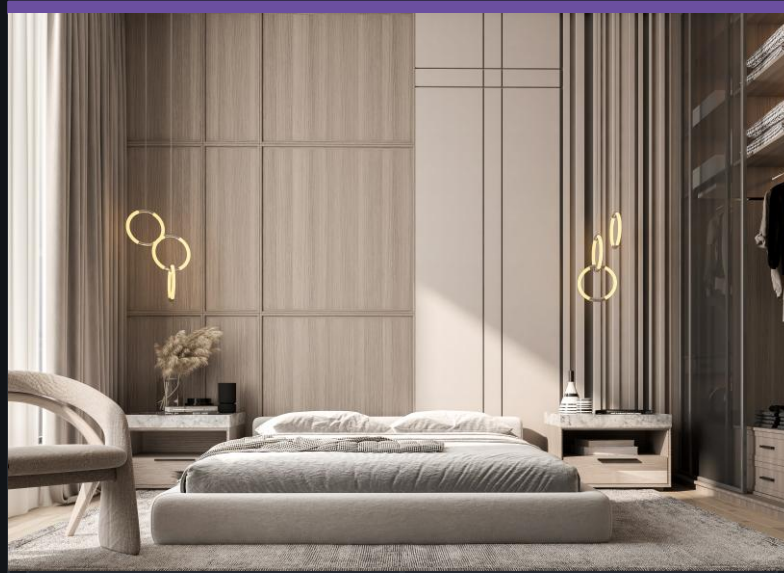

Guest Bedroom

Neutral & warm tones



Children's Room

Playful & creative

Interior Design — Detail & Material Shots



Cozy Living Room



Warm textures & soft lighting



Rest-Reading Zone

Focused ambiance design



Bathroom — Luxury Finish



Stone & glass details



Private Office Space



Functional contemporary

Interior Design — Chosen Renders



Luxury Master Suite

NEO CLASSIC



DINNING ROOM

Neutral & warm tones



DINNING ROOM

Neutral & warm tones

Interior Design — Detail & Material Shots



Cozy Living Room



Warm textures & soft lighting



Rest-Reading Zone



Focused ambiance design



RETAIL — Luxury Finish



Stone & glass details



Private Office Space



Functional contemporary

SKILLS OVERVIEW

BIM · Shop Drawings · Healthcare BIM · Exterior & Interior · Landscape

DOCUMENTATION Floor Plans (LOD 350) Exploded Axonometrics Sections A-A/B-B 4 Elevations + Details As-Built Docs Licensing Sets	3D & MODELING 3D Arch Models Custom Families Parametric Assemblies 4D Construction Seq. 5D BOQ Integration IFC Export	COORDINATION Navisworks NWD Setup Multi-Disc. Clash Tests Clash Report Gen. Issue & Resolution Log BCF Export/Import Zero-Clash Sign-Off	DATA & SCHEDULES Room Finish Sched. Automated BOQ Material Takeoff Door/Window Sched. Area & Volume Rep. Parameter Mapping
CLOUD & CDE BIM 360 / ACC Setup ISO 19650 Compliance Document Status Codes WIP→Shared→Published RFI & Issue Tracking Transmittal Mgmt	STANDARDS ISO 19650-1 & -2 BEP Development OIR / AIR Req. LOD Matrix Def. BIM Protocol Setup Info Delivery Plan	SHOP DRAWINGS Arch. Floor Plans Building Sections All 4 Elevations Wall & Facade Details 3D Axonometric Views Licensing Packages	HEALTHCARE BIM Institutional Facility BIM LOD 350+ Medical Models MEP Coordination Vision 2030 Aligned Supply Chain Project Design-to-Procurement

LET'S WORK TOGETHER.

Open to remote, hybrid, and part-time engagements.

Available GMT+2 — Flexible for EST, PST & GMT schedules.

Email architect.abdelrhmanmohsen@gmail.com

LinkedIn linkedin.com/in/abdelrhman-mohsen-bimarchitect

Phone +201092083829



ABDELRHMAN MOHSEN

BIM Architect & Coordinator · Egypt · UAE · KSA